PLANTA GENERALIS

HOSPITALIS MEDIOLANENSIS

SEC. XVI

Disposttio perpetua.

INSITUTUM CLINICUM MEDIOLANI

MEDICINA · SCIENTIA · CURA

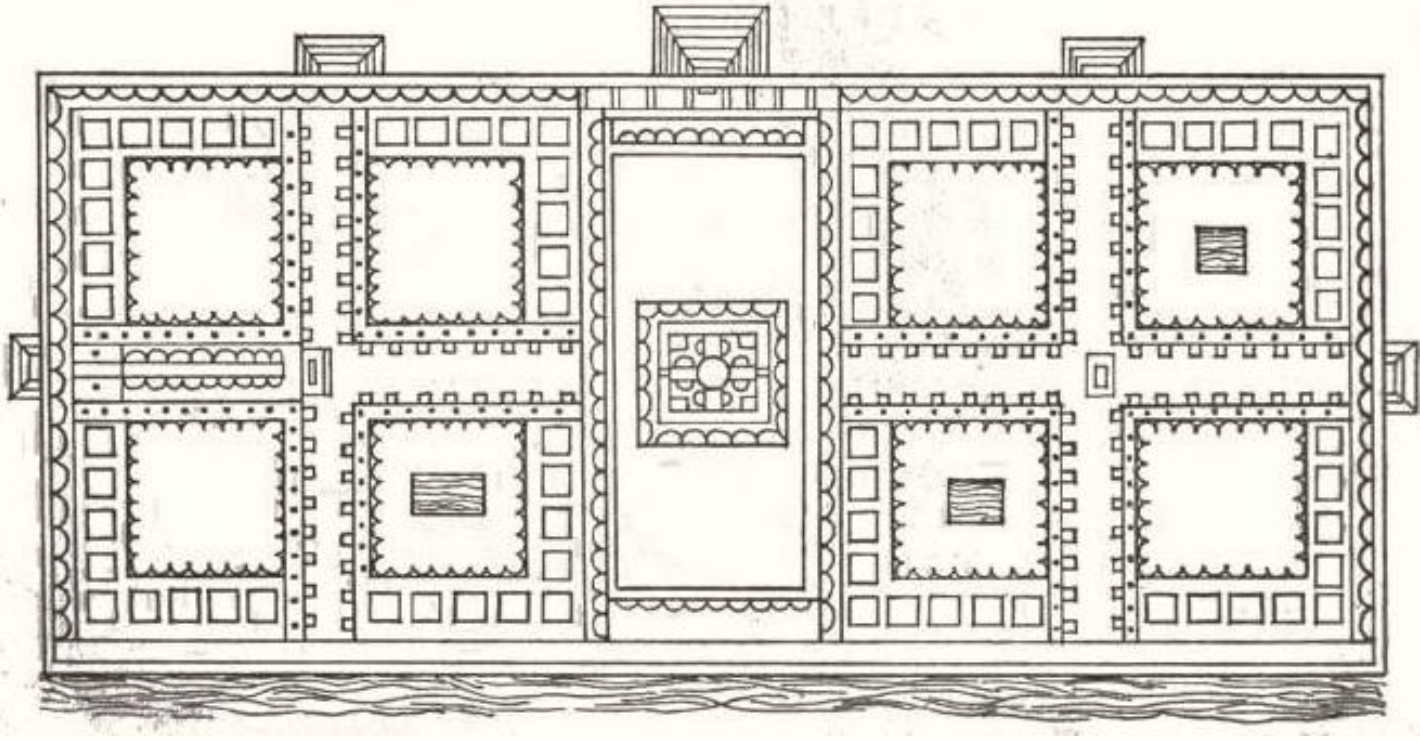

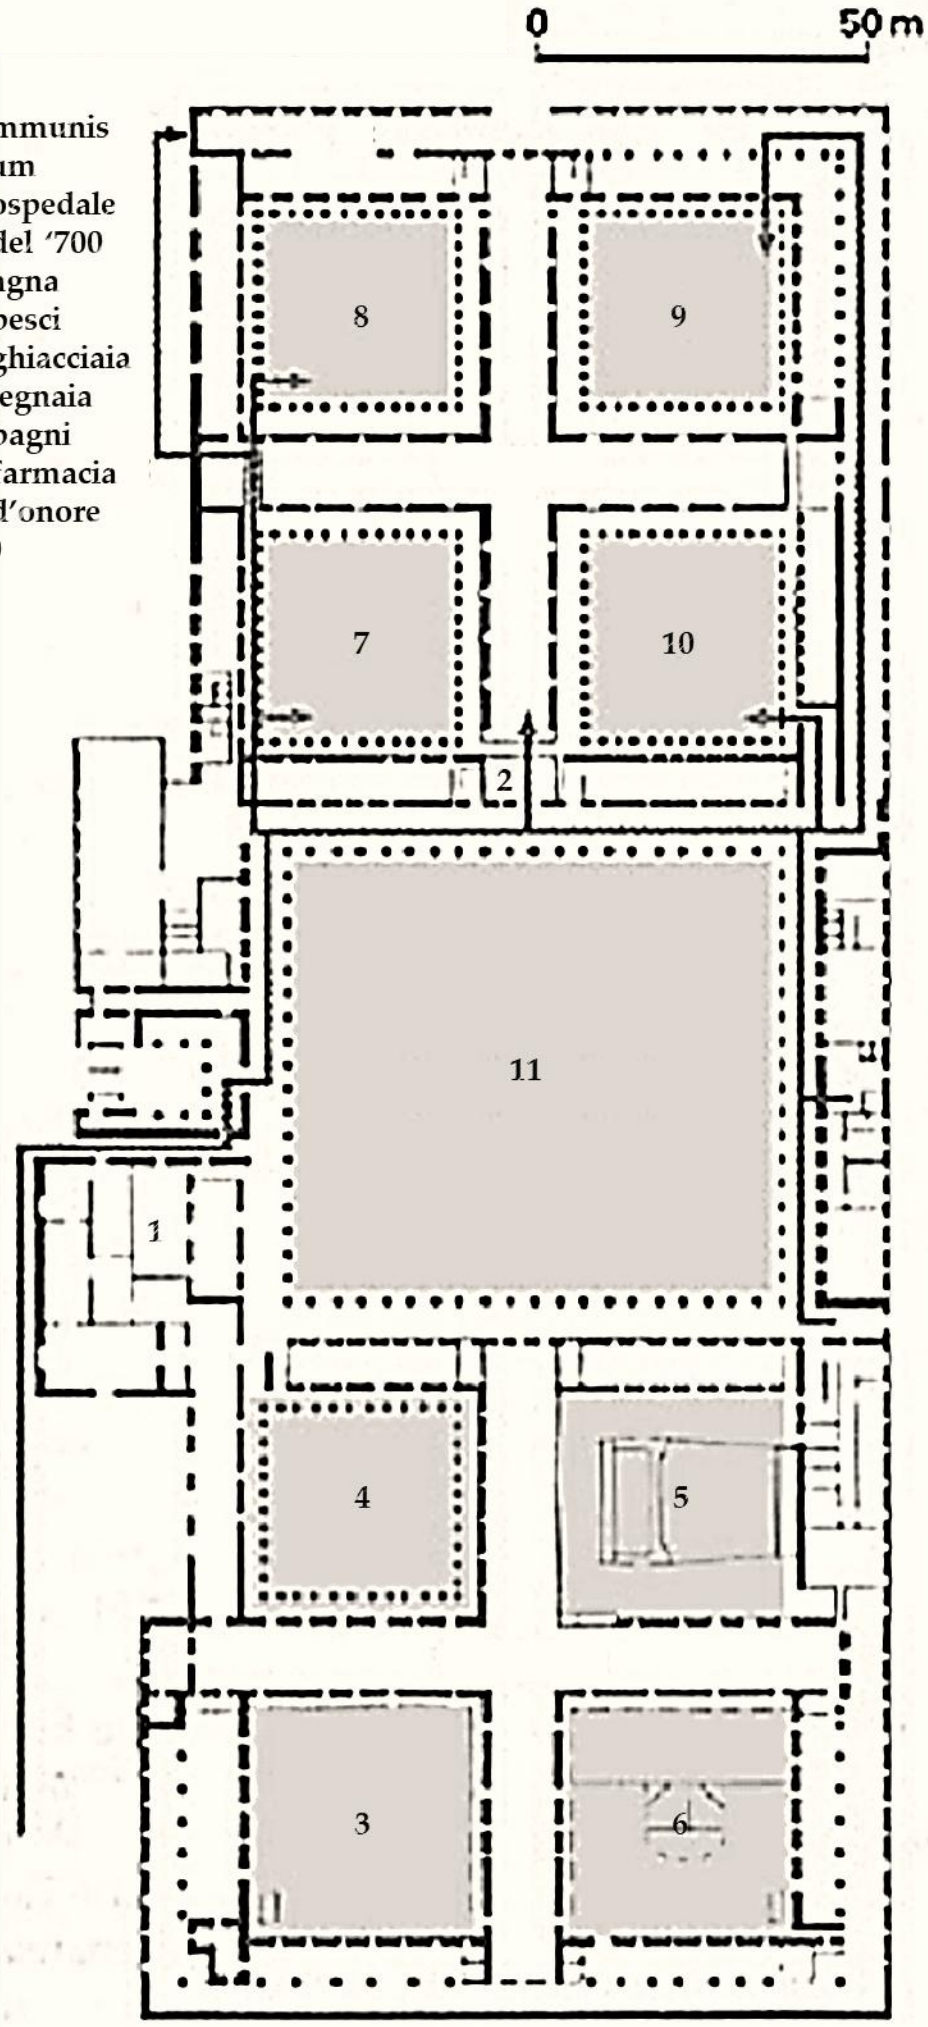
0
50 m
1. area communis
2. archivium
3. cortile ospedale
4. cortile del '700
5. aula magna
6. cortile pesci
7. cortile ghiacciaia
8. cortile legnaia
9. cortile bagni
10. cortile farmacia
11. cortile d'onore del '600
8
9
7
10
2
11
1
4
5
3
6

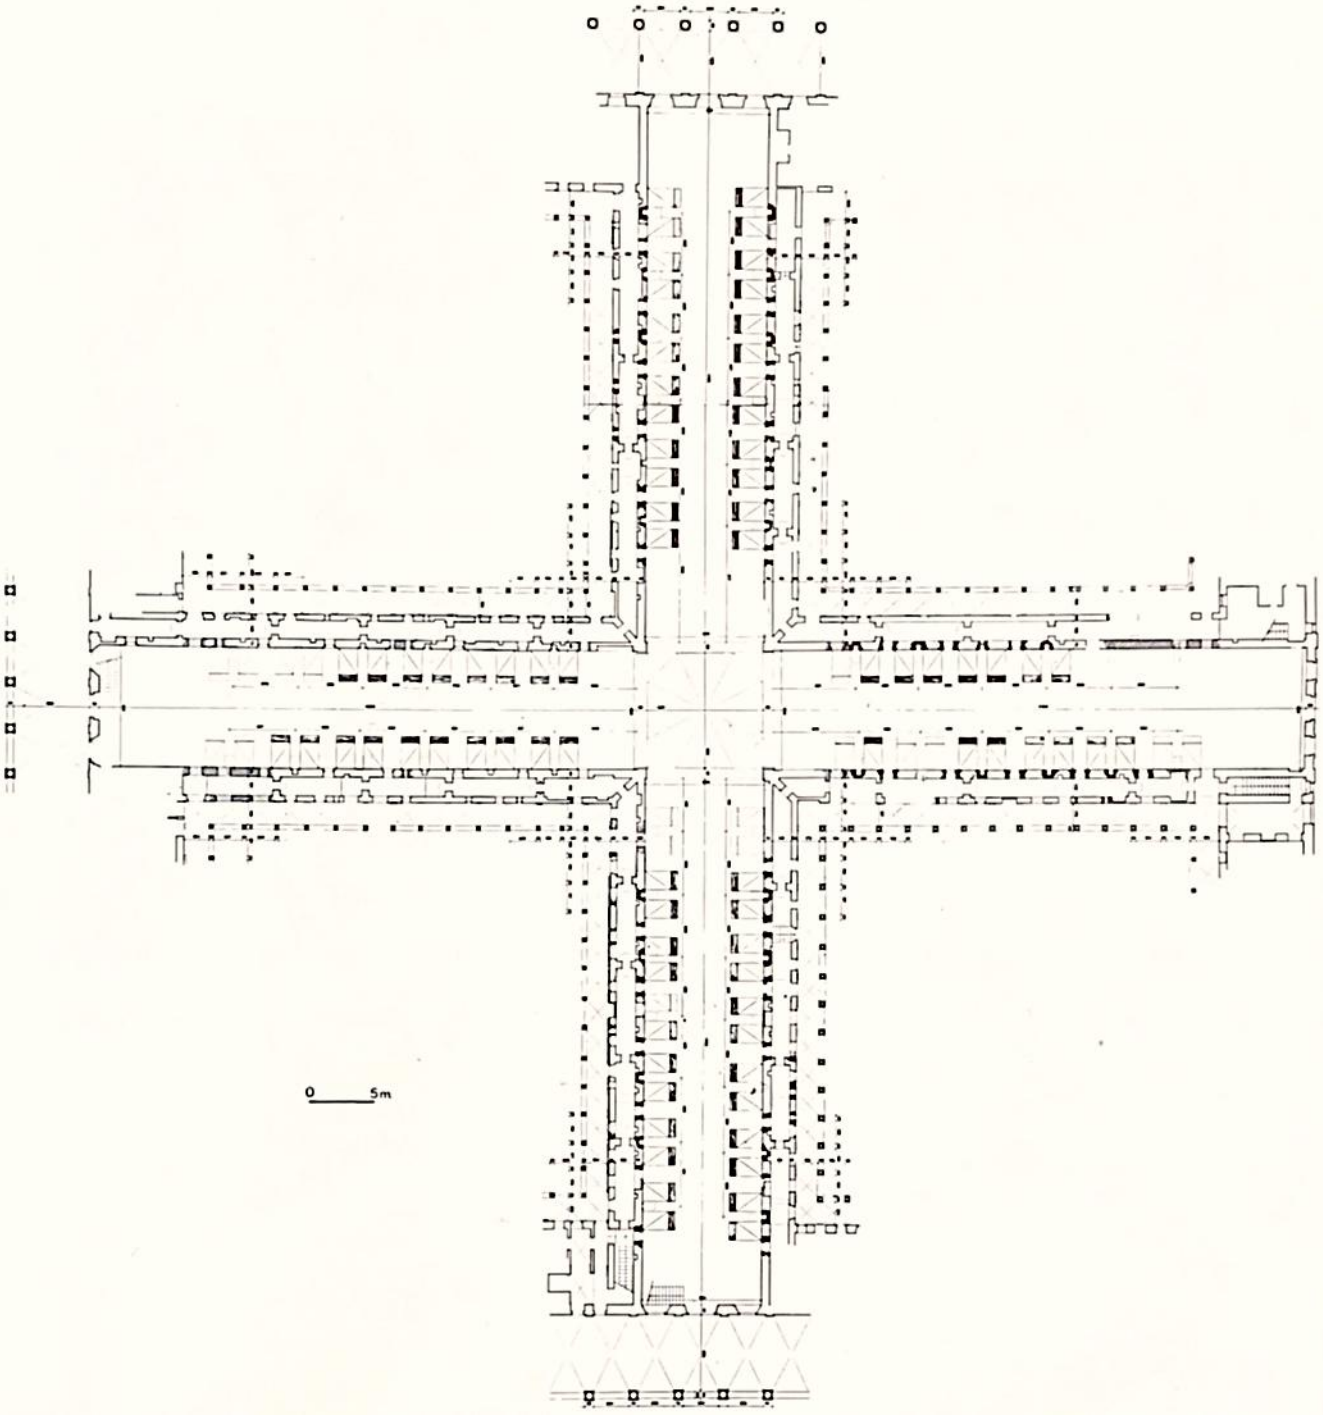

Pianta del piano superiore della crociera sforzesca con tracce delle aperture originali e posizione dei letti