L'assetto medievale intorno alla Basilica di Santa Tecla a Milano

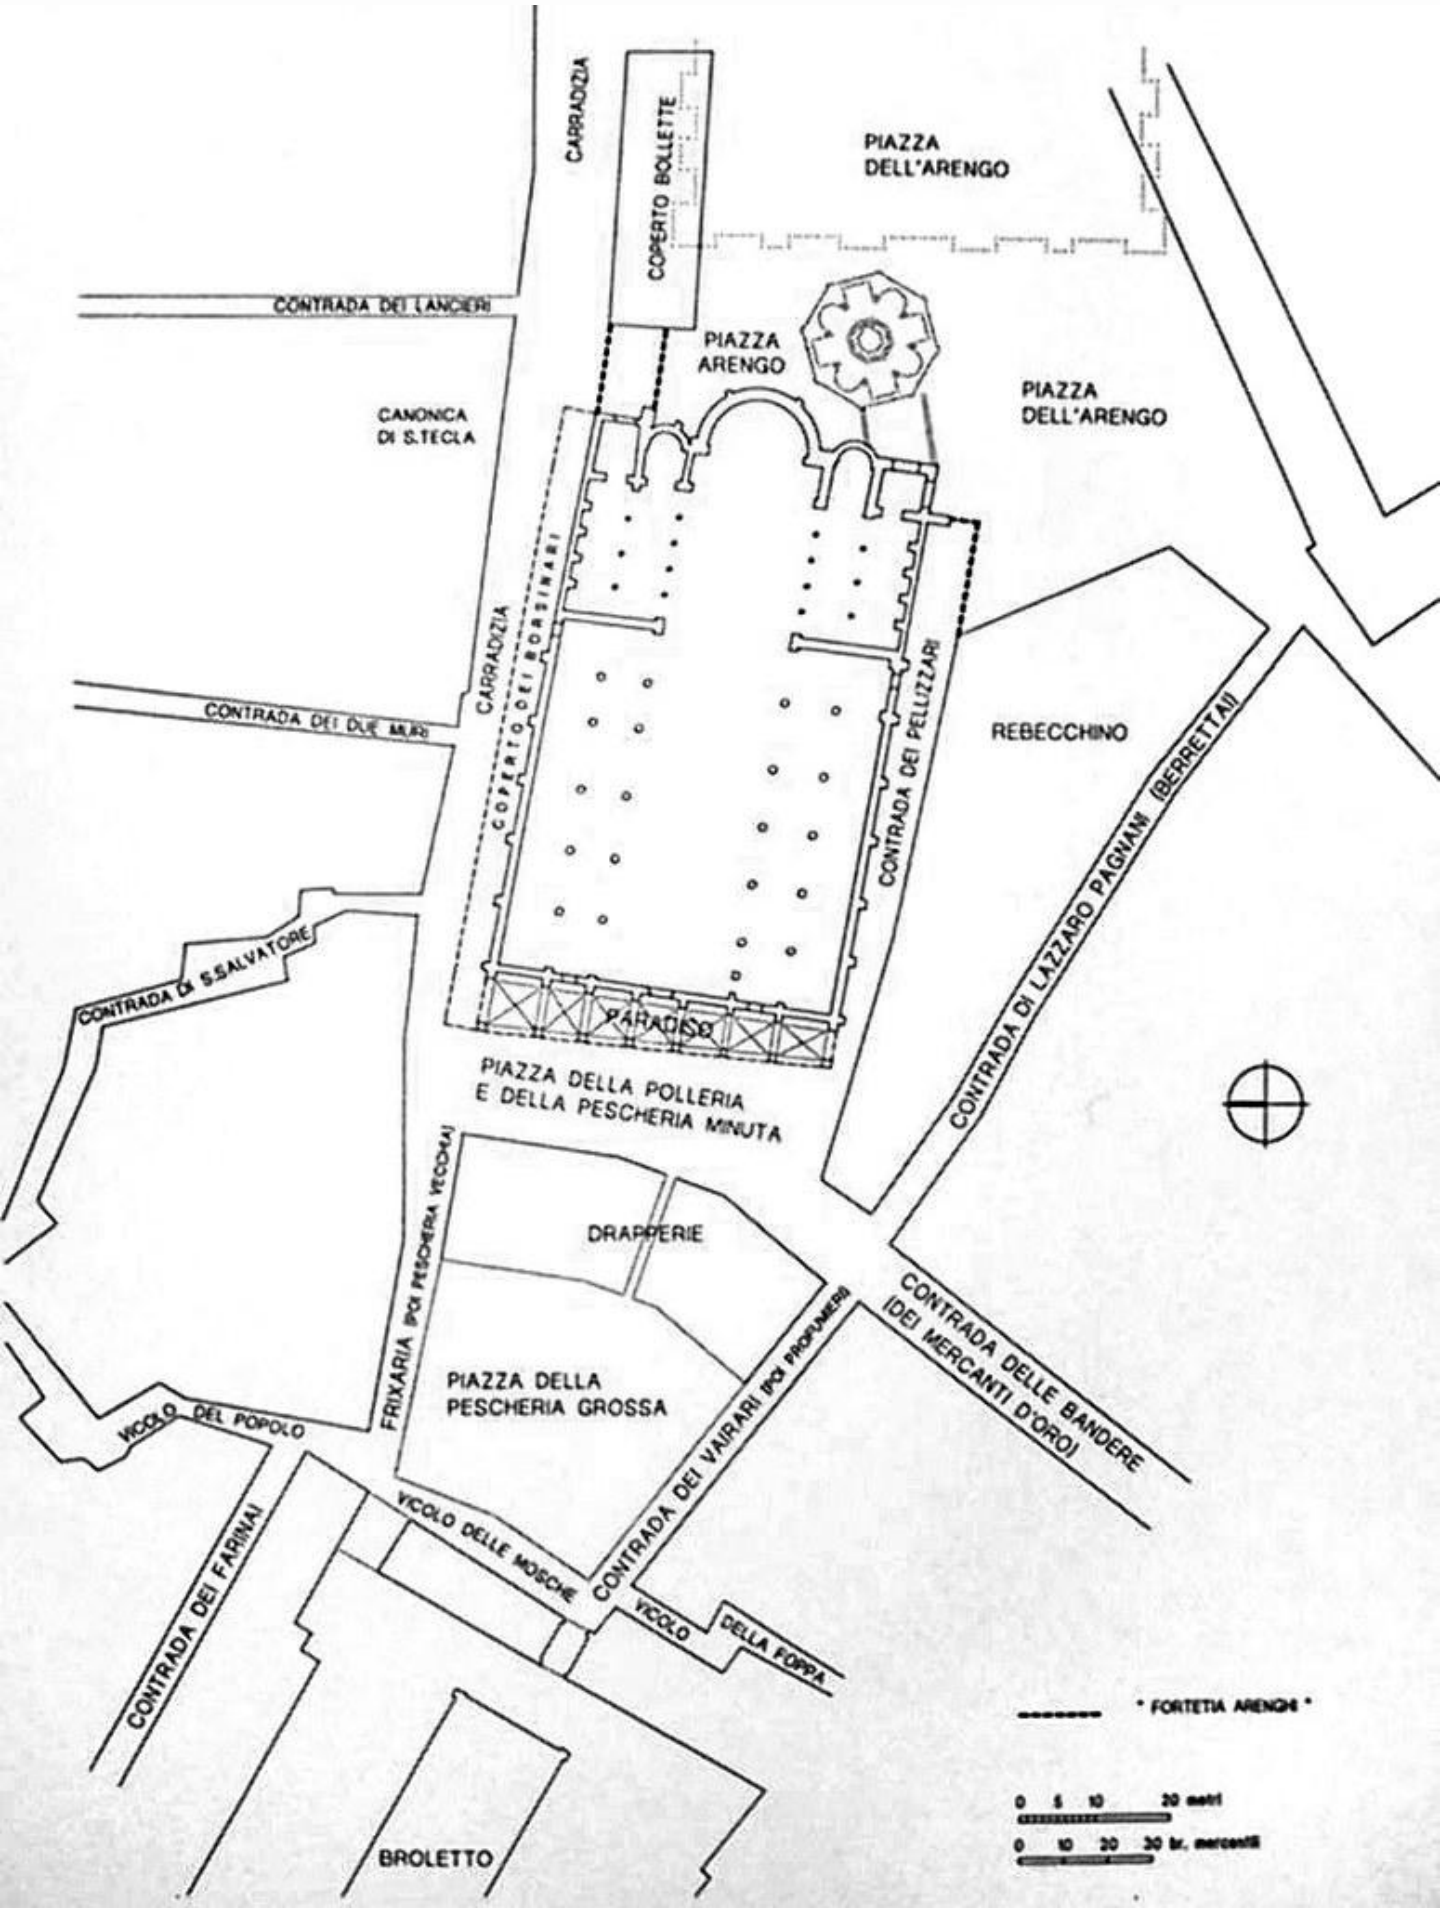

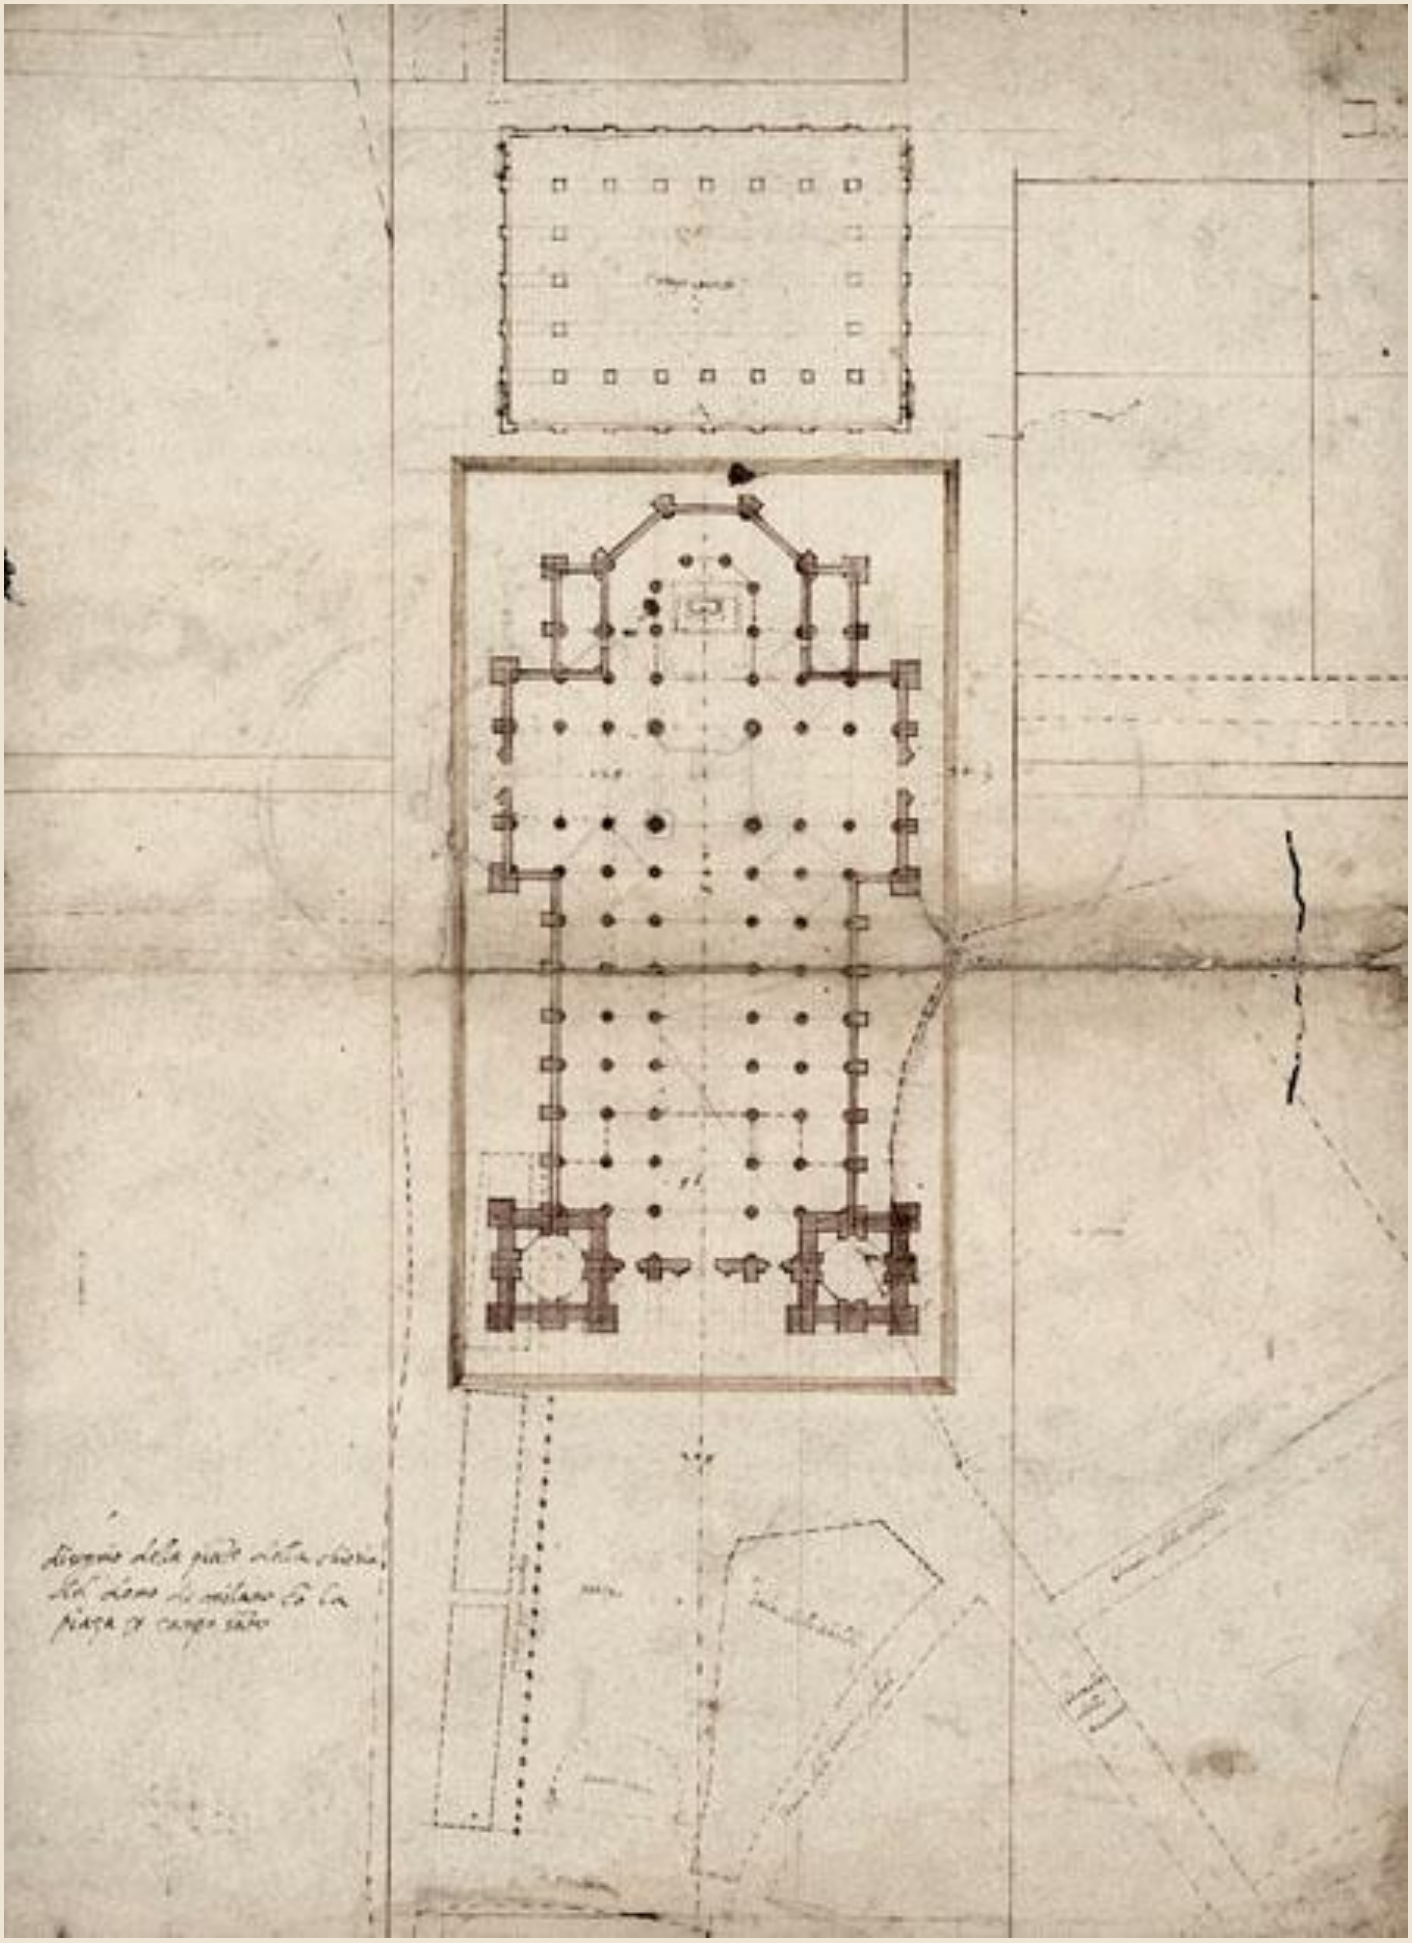

Progetto di Vincenzo Seregni, 1548, non realizzato (*Milano – Castello Sforzesco. Biblioteca Trivulziana, Archivio storico, Raccolta Bianconi, Tomo II, A4057*)

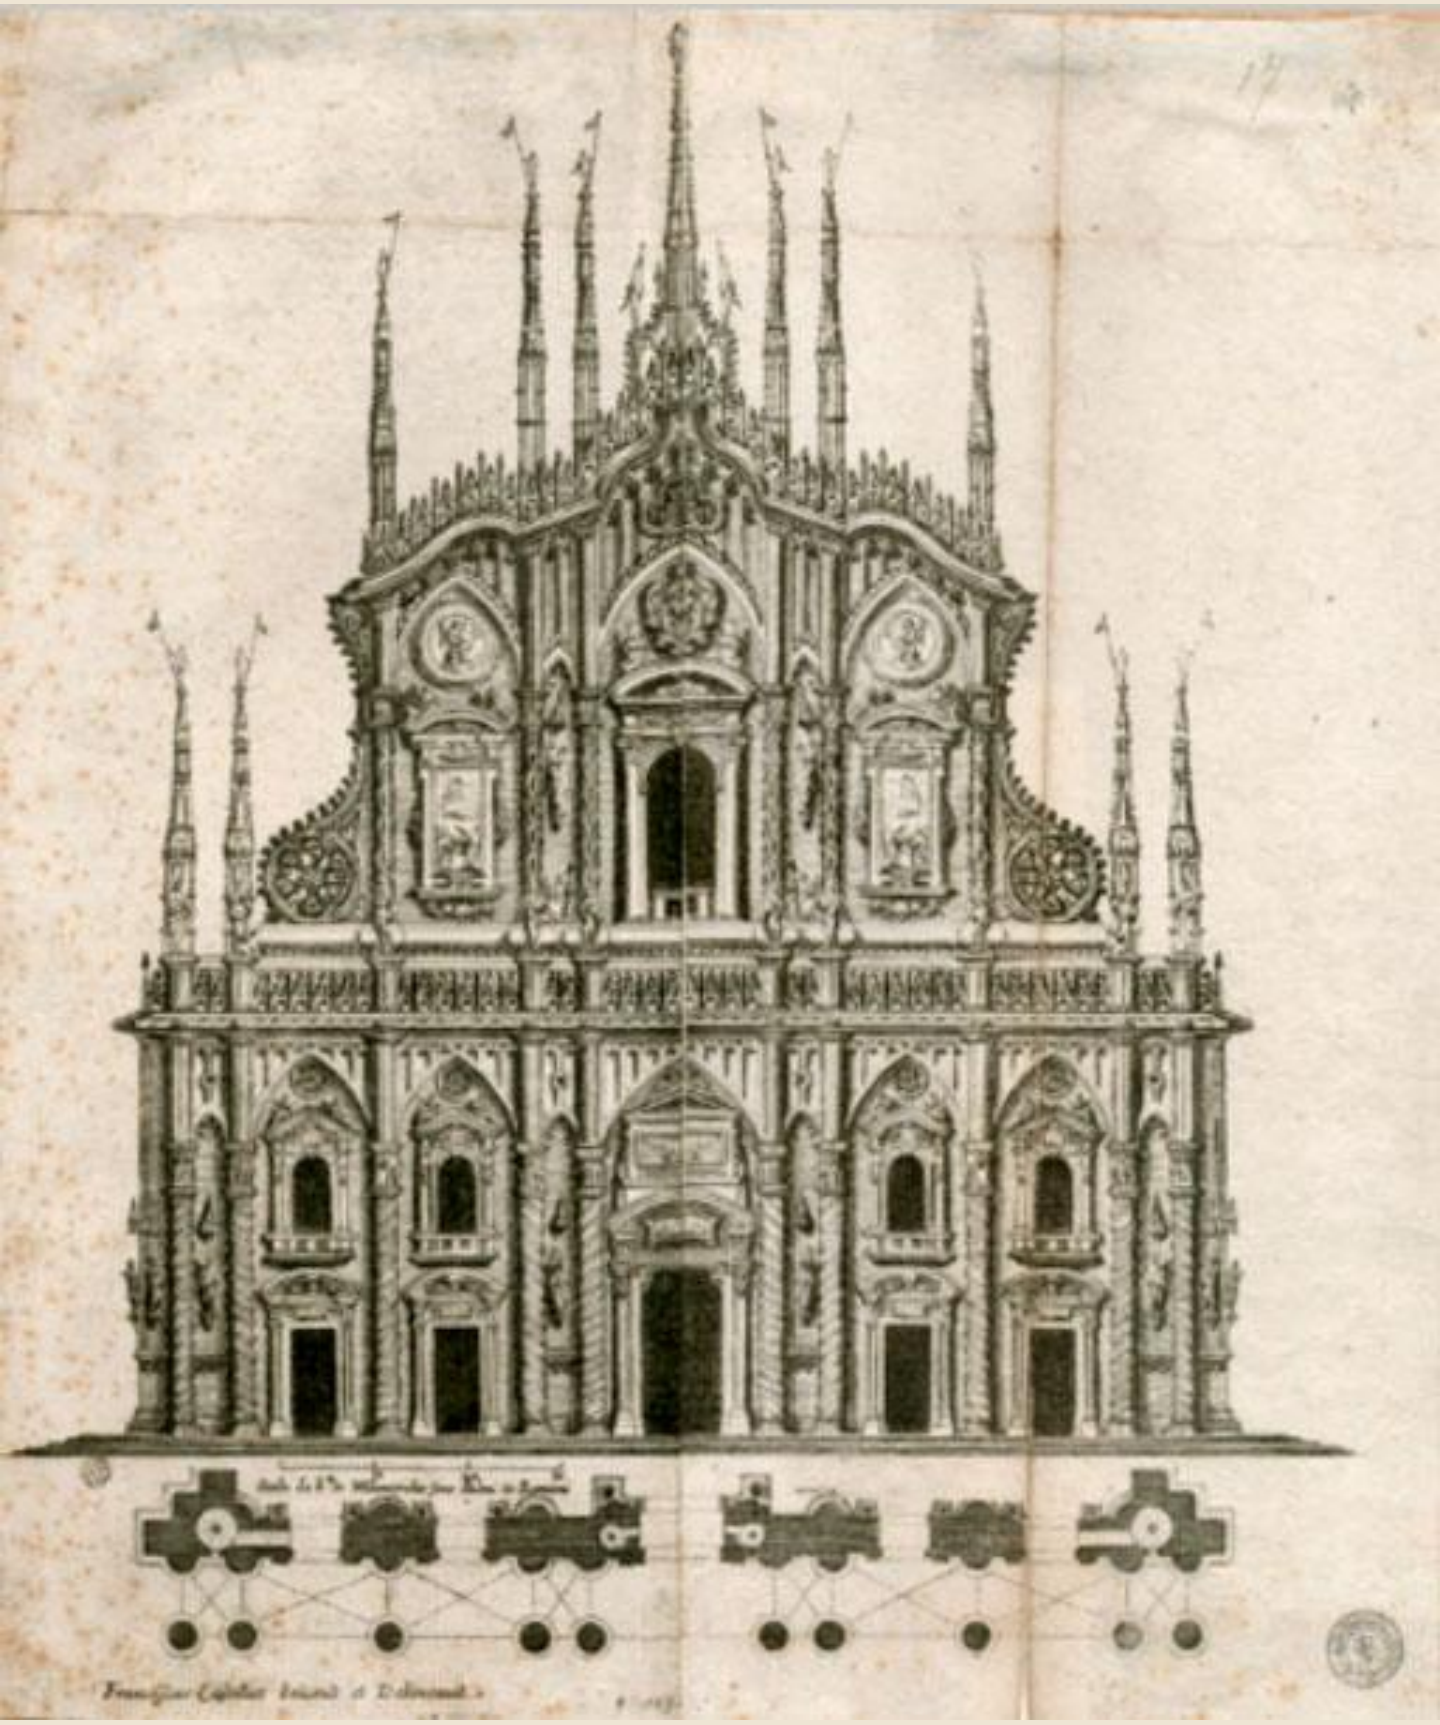

Progetto di Francesco Castelli, 1650, non realizzato. Il fronte proposto è un ibrido tra il gotico e il "romano", con colonne tortili e guglie di ispirazione barocca (*Milano, Civica Raccolta delle Stampe Achille Bertarelli – P.V. m. 8-17*)

Progetto di Luigi Vanvitelli, 1745, non realizzato.
(*Milano, Civica Raccolta delle Stampe Achille Bertarelli – P.V. m. 8-19*)

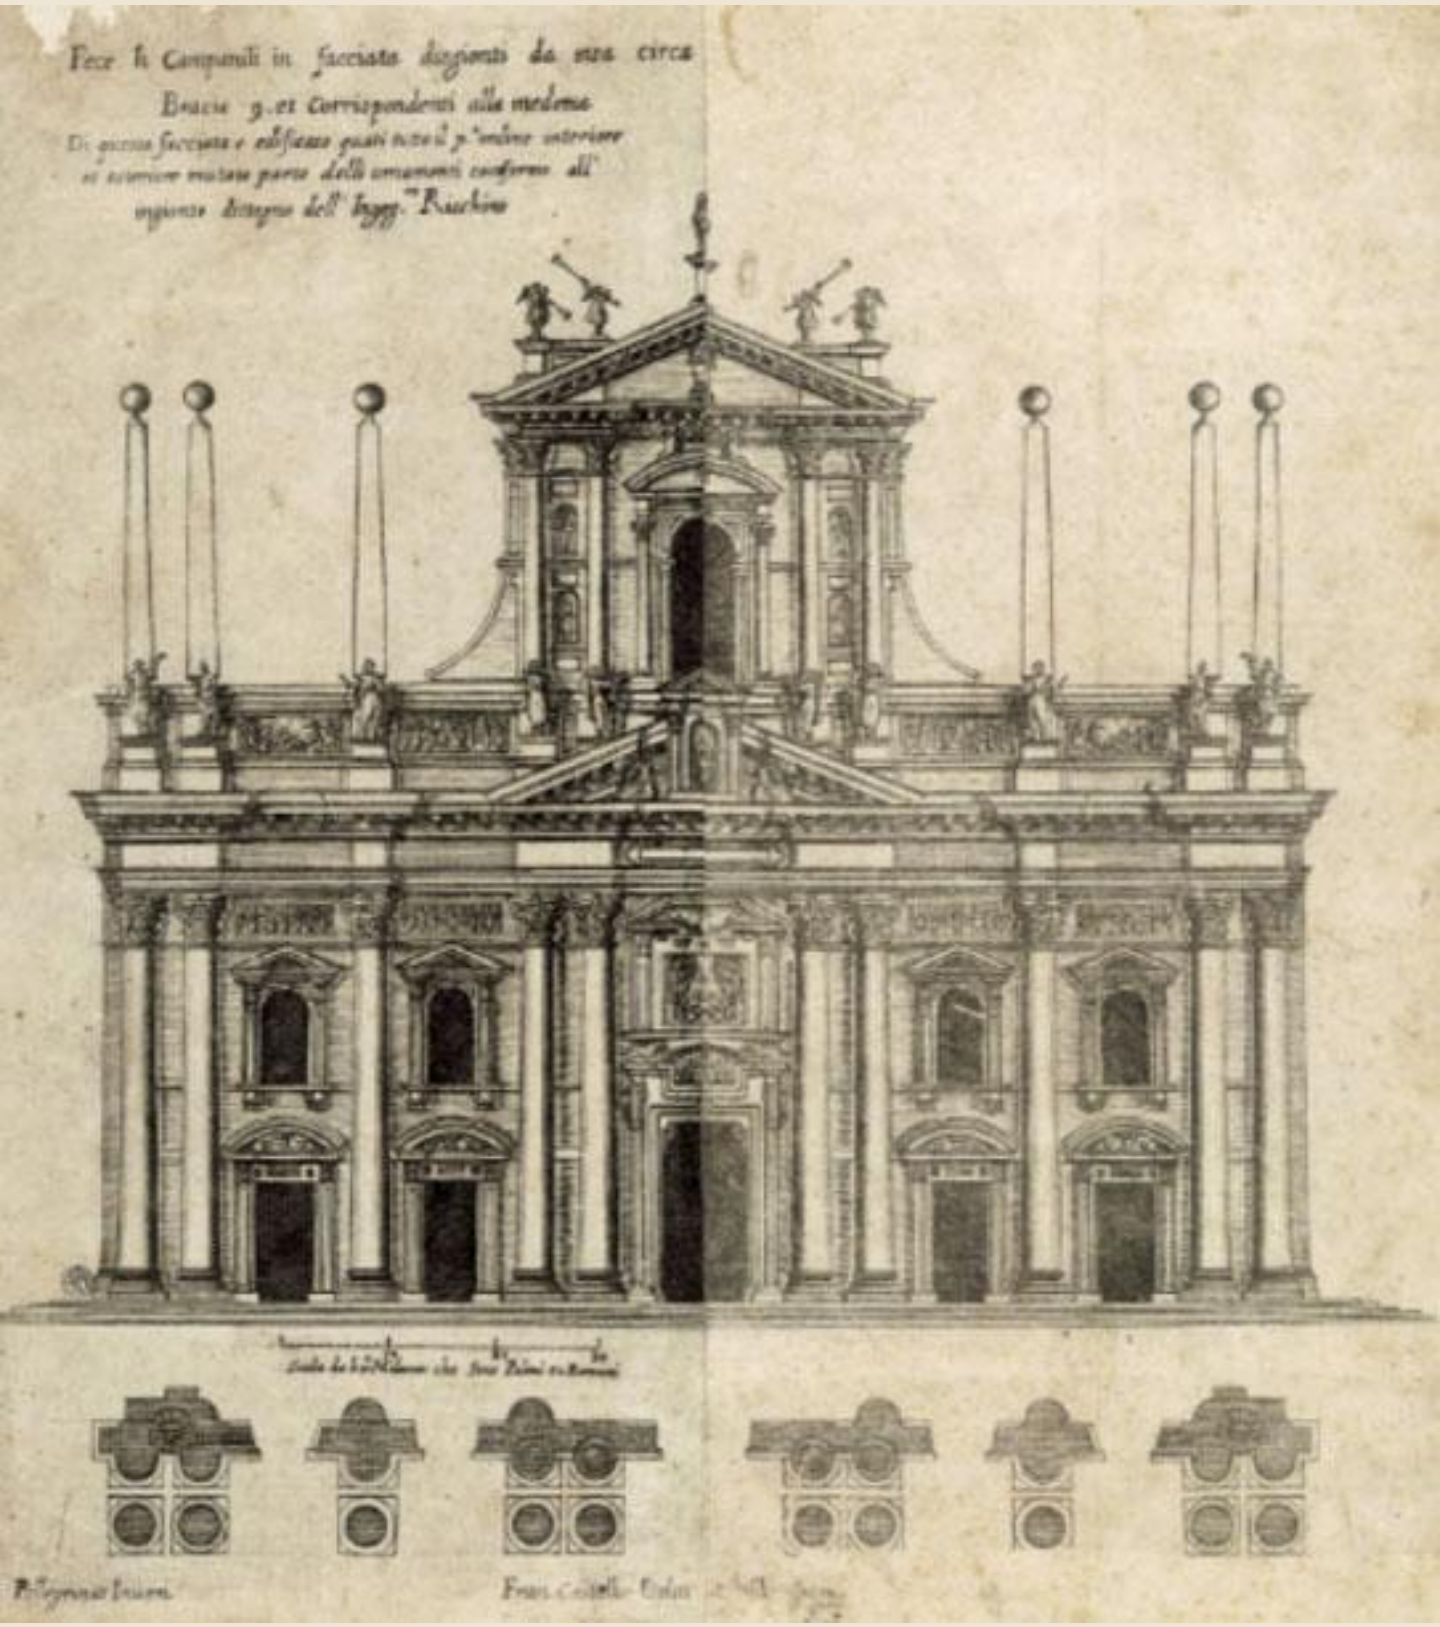

Progetto di Pellegrino Tibaldi, 1571, non realizzato. Il fronte proposto presenta un'architettura ispirata al gusto "romano" che suscita numerose polemiche (*Milano – Civica Raccolta delle Stampe Achille Bertarelli – P.V. m. 8-12*)