PLANTA GENERALIS

HOSPITALIS MEDIOLANENSIS

SEC. XVI

Dispositio perpetua.

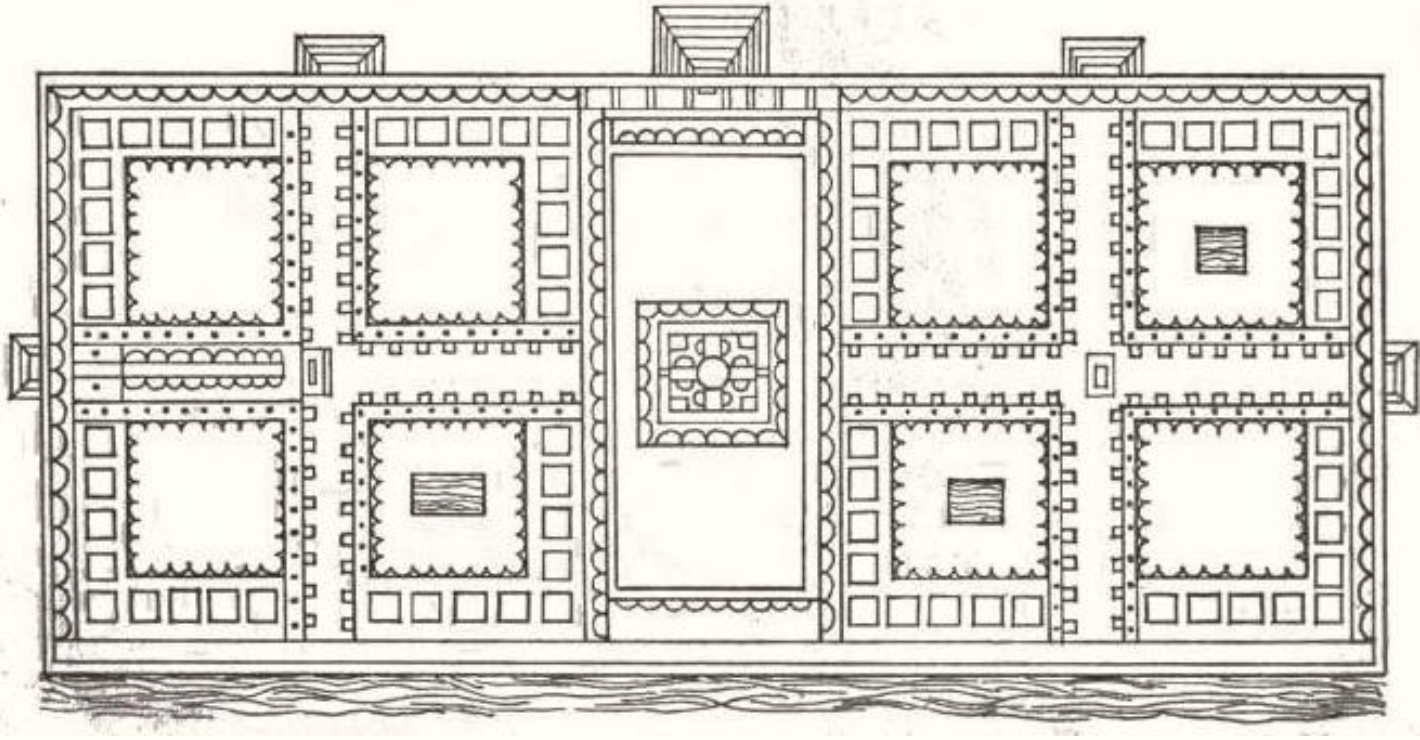

1. area communis
2. archivium
3. cortile ospedale
4. cortile del '700
5. aula magna
6. cortile pesci
7. cortile ghiacciaia
8. cortile legnaia
9. cortile bagni
10. cortile farmacia
11. cortile d'onore del '600

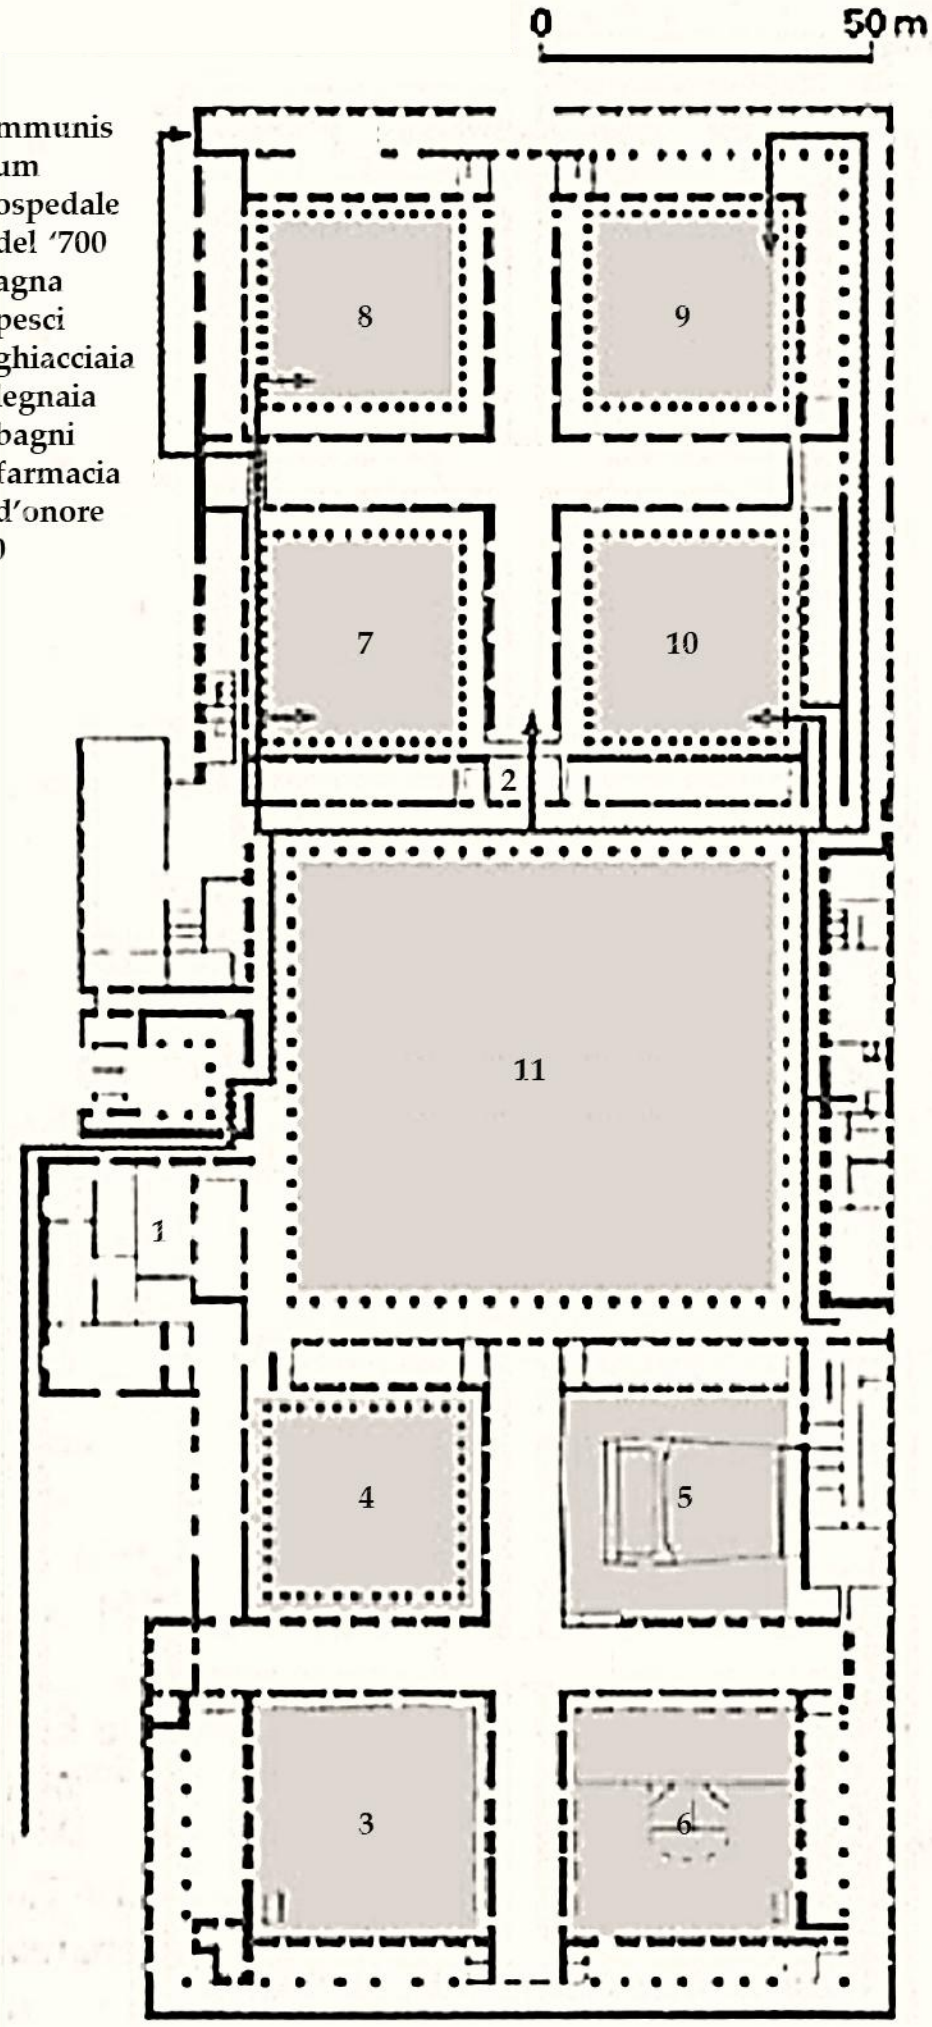

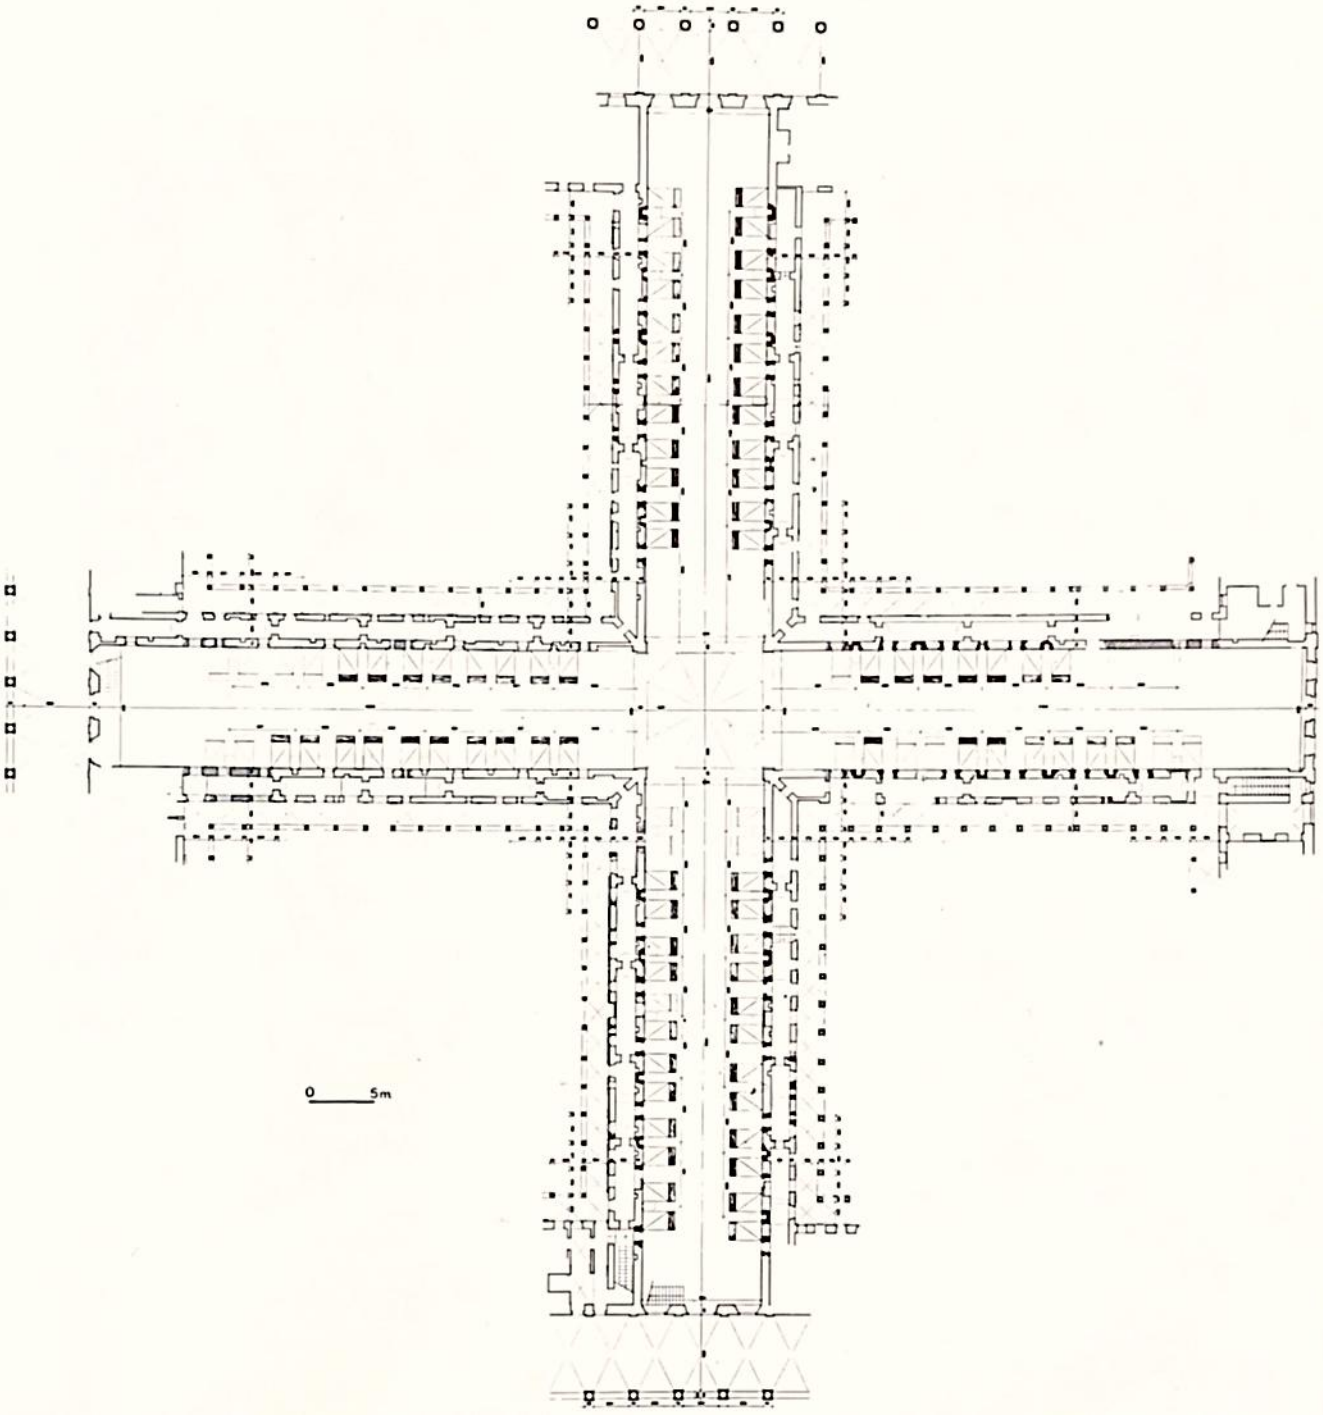

Pianta del piano superiore della crociera sforzesca con tracce delle aperture originali e posizione dei letti