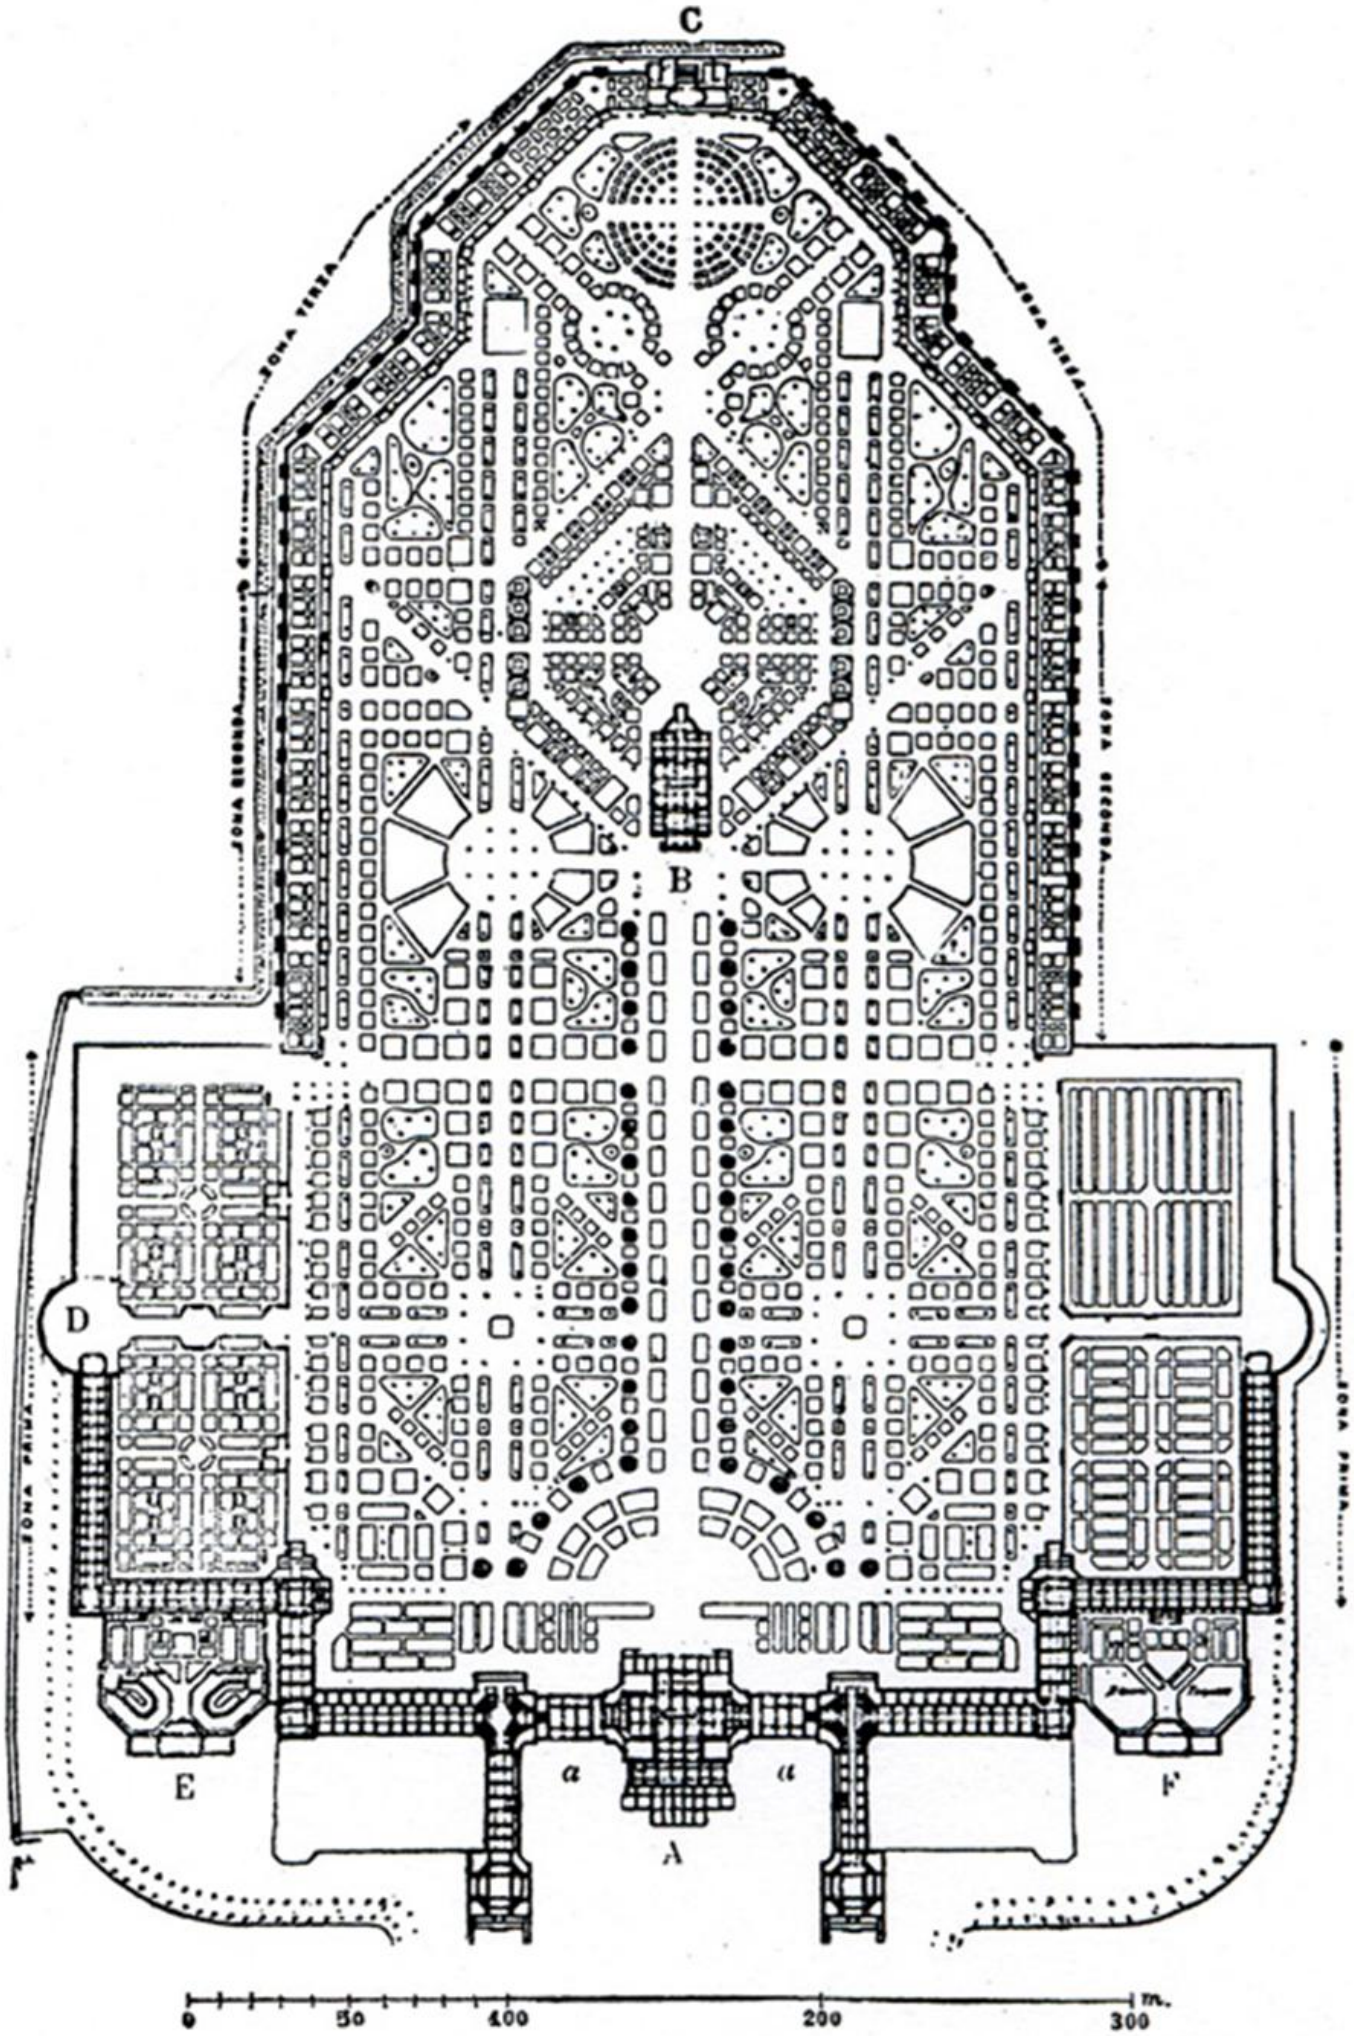

Fig. 716. — Planimetria generale (arch. C. Maciachini).

PROSPETTO CENTRALE ESTERNO DELLA FACCIATA.
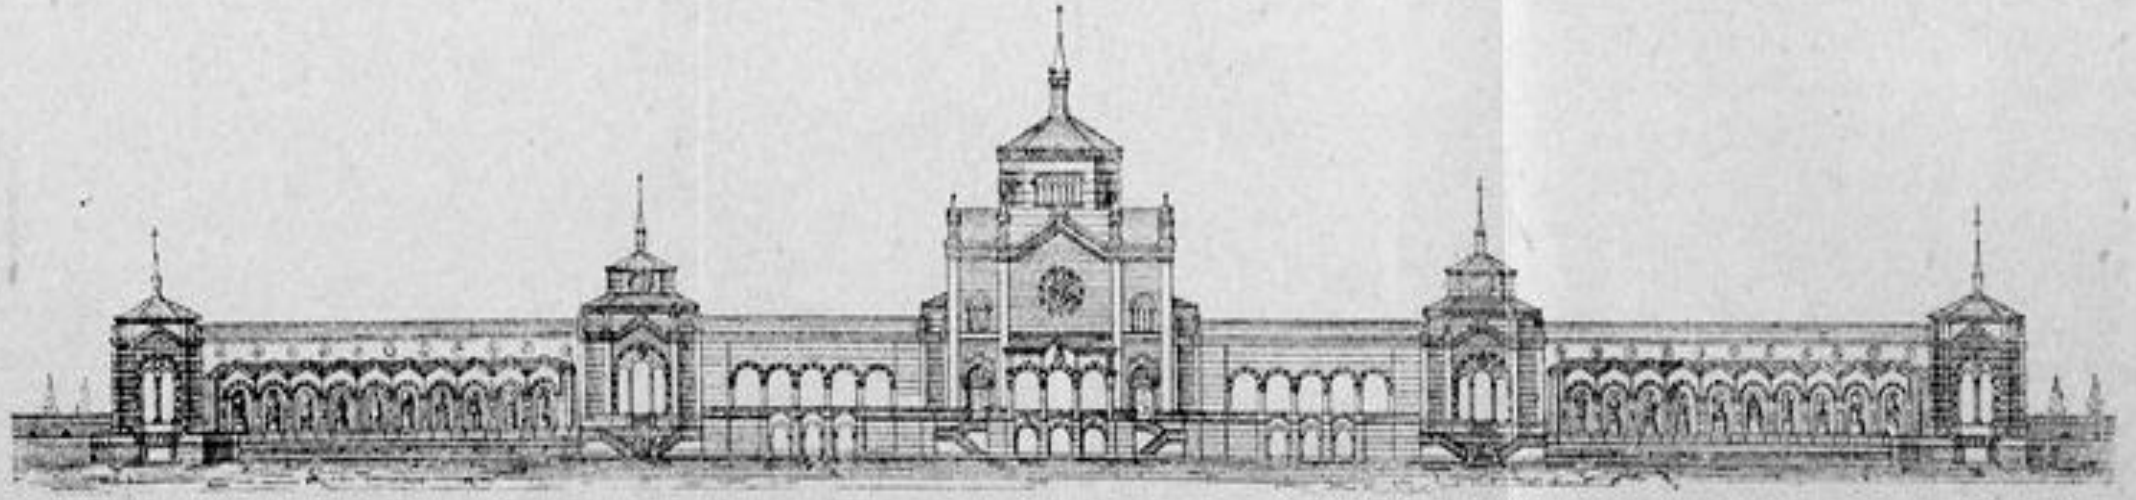
PROSPETTO CENTRALE INTERNO DELLA FACCIATA.